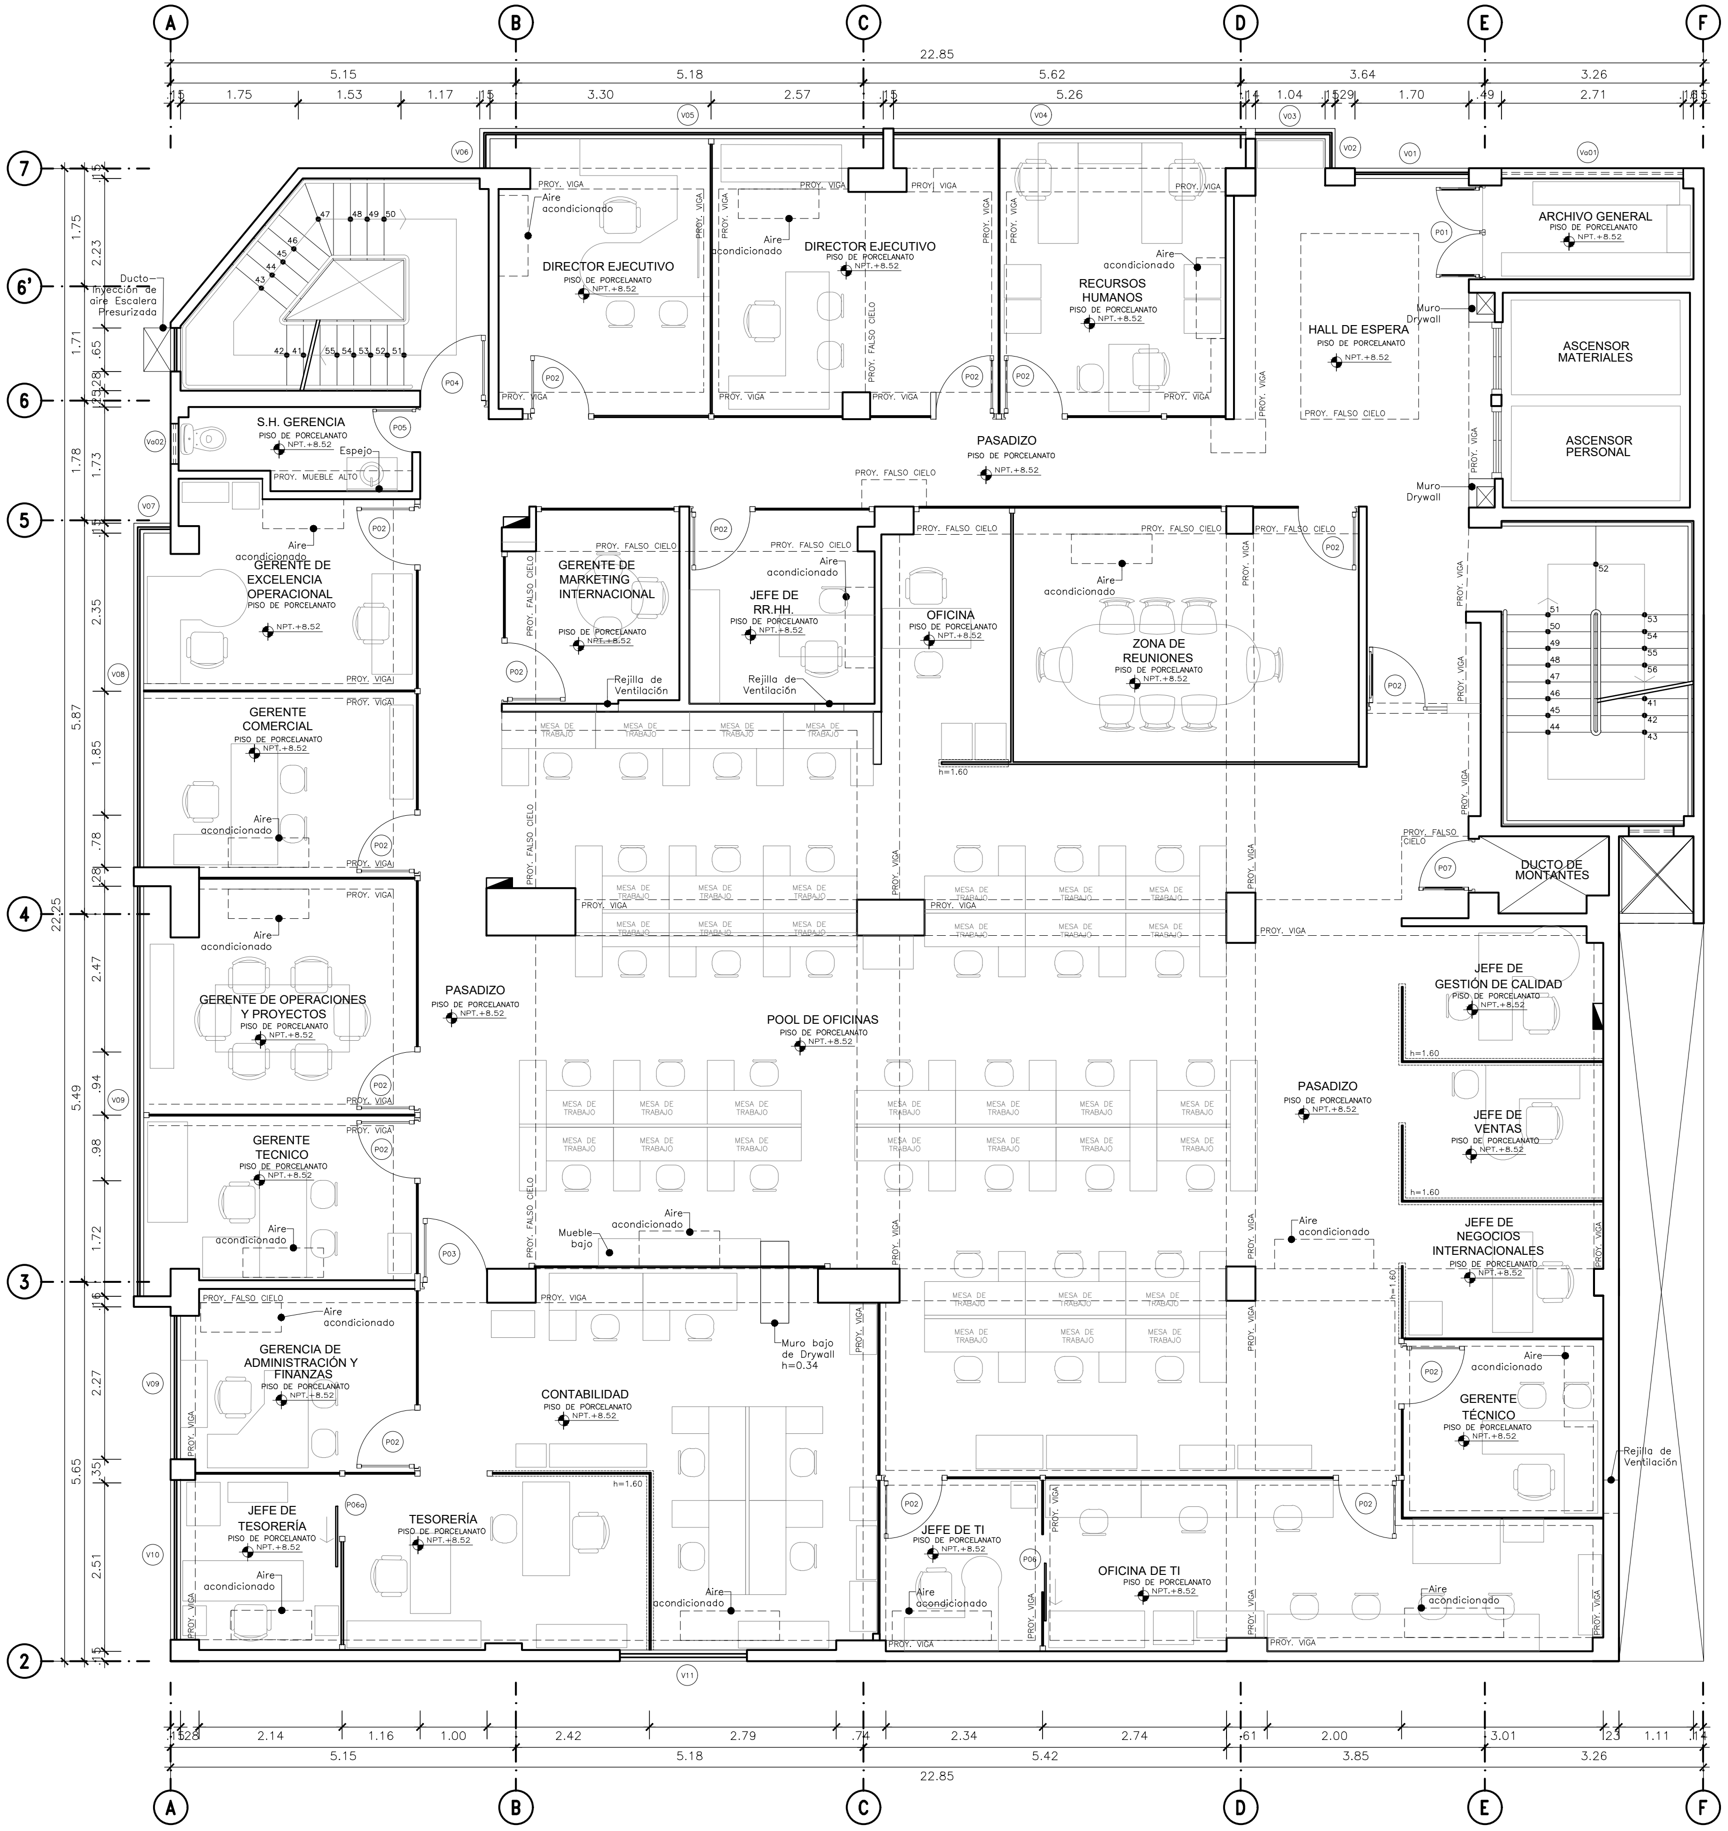
A
B
C
D
E
F
7
6'
6
5
4
3
2
22.85
5.15
5.18
5.62
3.64
3.26
1.75
1.53
1.17
3.30
2.57
5.26
1.04
1.70
2.71
2.14
1.16
1.00
2.42
2.79
.74
2.34
2.74
.61
2.00
3.01
1.11
5.42
3.85
22.25
2.23
1.71
.65
1.78
1.73
5.87
2.35
1.85
.78
2.47
5.49
.94
.98
1.72
5.65
2.27
2.51
Ducto Inyección de aire Escalera Presurizada
S.H. GERENCIA
PISO DE PORCELANATO
NPT.+8.52
Espejo
PROY. MUEBLE ALTO
DIRECTOR EJECUTIVO
PISO DE PORCELANATO
NPT.+8.52
Aire acondicionado
PROY. VIGA
PROY. FALSO CIELO
DIRECTOR EJECUTIVO
PISO DE PORCELANATO
NPT.+8.52
RECURSOS HUMANOS
PISO DE PORCELANATO
NPT.+8.52
PASADIZO
PISO DE PORCELANATO
NPT.+8.52
HALL DE ESPERA
PISO DE PORCELANATO
NPT.+8.52
ARCHIVO GENERAL
PISO DE PORCELANATO
NPT.+8.52
Muro Drywall
ASCENSOR MATERIALES
ASCENSOR PERSONAL
GERENTE DE EXCELENCIA OPERACIONAL
PISO DE PORCELANATO
NPT.+8.52
GERENTE DE MARKETING INTERNACIONAL
PISO DE PORCELANATO
NPT.+8.52
Rejilla de Ventilación
JEFE DE RR.HH.
PISO DE PORCELANATO
NPT.+8.52
OFICINA
PISO DE PORCELANATO
NPT.+8.52
ZONA DE REUNIONES
PISO DE PORCELANATO
NPT.+8.52
h=1.60
GERENTE COMERCIAL
PISO DE PORCELANATO
NPT.+8.52
MESA DE TRABAJO
DUCTO DE MONTANTES
GERENTE DE OPERACIONES Y PROYECTOS
PISO DE PORCELANATO
NPT.+8.52
PASADIZO
PISO DE PORCELANATO
NPT.+8.52
POOL DE OFICINAS
PISO DE PORCELANATO
NPT.+8.52
JEFE DE GESTIÓN DE CALIDAD
PISO DE PORCELANATO
NPT.+8.52
PASADIZO
PISO DE PORCELANATO
NPT.+8.52
JEFE DE VENTAS
PISO DE PORCELANATO
NPT.+8.52
GERENTE TECNICO
PISO DE PORCELANATO
NPT.+8.52
Mueble bajo
JEFE DE NEGOCIOS INTERNACIONALES
PISO DE PORCELANATO
NPT.+8.52
GERENCIA DE ADMINISTRACIÓN Y FINANZAS
PISO DE PORCELANATO
NPT.+8.52
Muro bajo de Drywall h=0.34
CONTABILIDAD
PISO DE PORCELANATO
NPT.+8.52
GERENTE TÉCNICO
PISO DE PORCELANATO
NPT.+8.52
Rejilla de Ventilación
JEFE DE TESORERÍA
PISO DE PORCELANATO
NPT.+8.52
TESORERÍA
PISO DE PORCELANATO
NPT.+8.52
JEFE DE TI
PISO DE PORCELANATO
NPT.+8.52
OFICINA DE TI
PISO DE PORCELANATO
NPT.+8.52
P01
P02
P03
P04
P05
P06
P07
V01
V02
V03
V04
V05
V06
V07
V08
V09
V10
V11